План 1 этажа

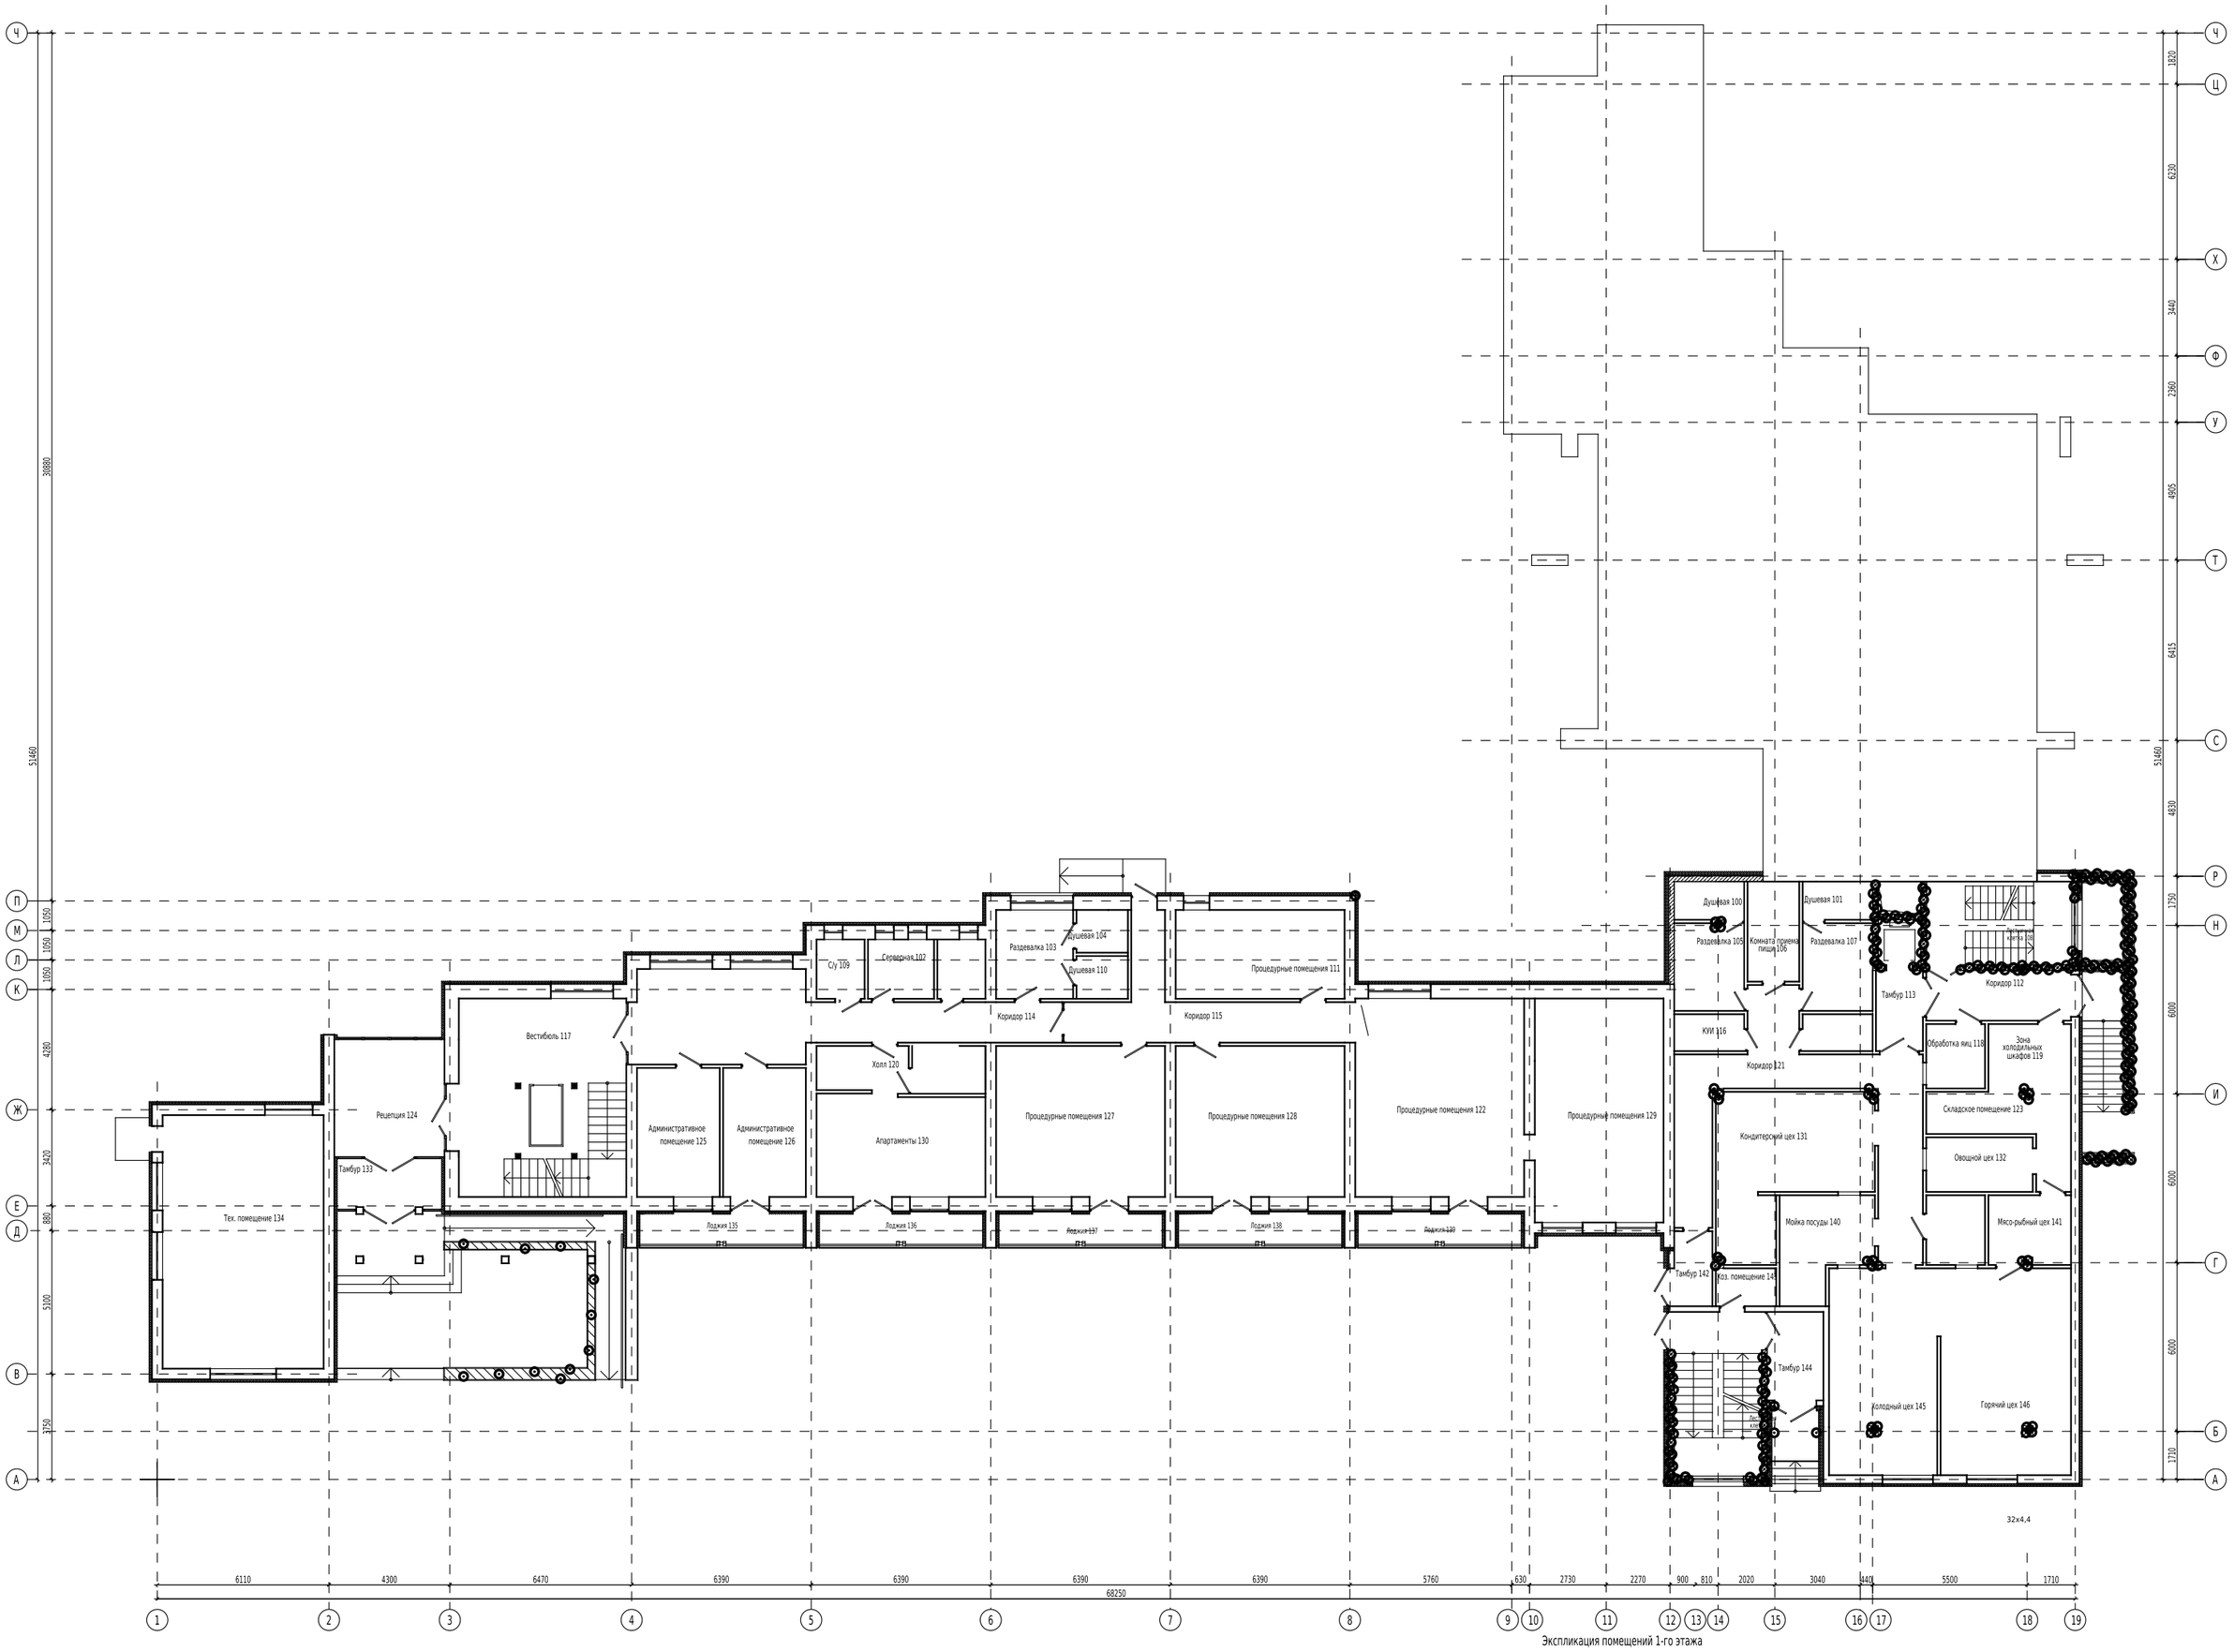

Экспликация помещений 1-го этажа

№	Наименование помещения	№	Наименование помещения	№	Наименование помещения	№	Наименование помещения
100	Душевая	112	Коридор	124	Рецепция	136	Лоджия
101	Душевая	113	Тамбур	125	Административное помещение	137	Лоджия
102	Серверная	114	Коридор	126	Административное помещение	138	Лоджия
103	Раздевалка	115	Коридор	127	Процедурные помещения	139	Лоджия
104	Душевая	116	КУИ	128	Процедурные помещения	140	Мойка посуды
105	Раздевалка	117	Вестибюль	129	Процедурные помещения	141	Мясо-рыбный цех
106	Комната приема пищи	118	Обработка яиц	130	Апартаменты	142	Тамбур
107	Раздевалка	119	Зона холодильных шкафов	131	Кондитерский цех	143	Хоз. помещение
108	Лестничная клетка	120	Холл	132	Овощной цех	144	Тамбур
109	СУ	121	Коридор	133	Тамбур	145	Холодный цех
110	Душевая	122	Процедурные помещения	134	Тех. помещение	146	Горячий цех
111	Процедурные помещения	123	Складское помещение	135	Лоджия	147	Лестничная клетка

1) Неуказанные диаметры трубопроводов системы отопления 20х2.8мм
2) Размещение радиаторов и полотенцесушителей уточнить по месту.
3) Трубопроводы отнесены от наружных стен условно, прокладку осуществить в полу и штробах.
4) На радиаторах установить вентили с термоголовками.
5) В местах прохода трубопроводами стен, перегородок установить стальные гильзы.

Взам. инв. N
Подпись и дата
Инв. N подл.

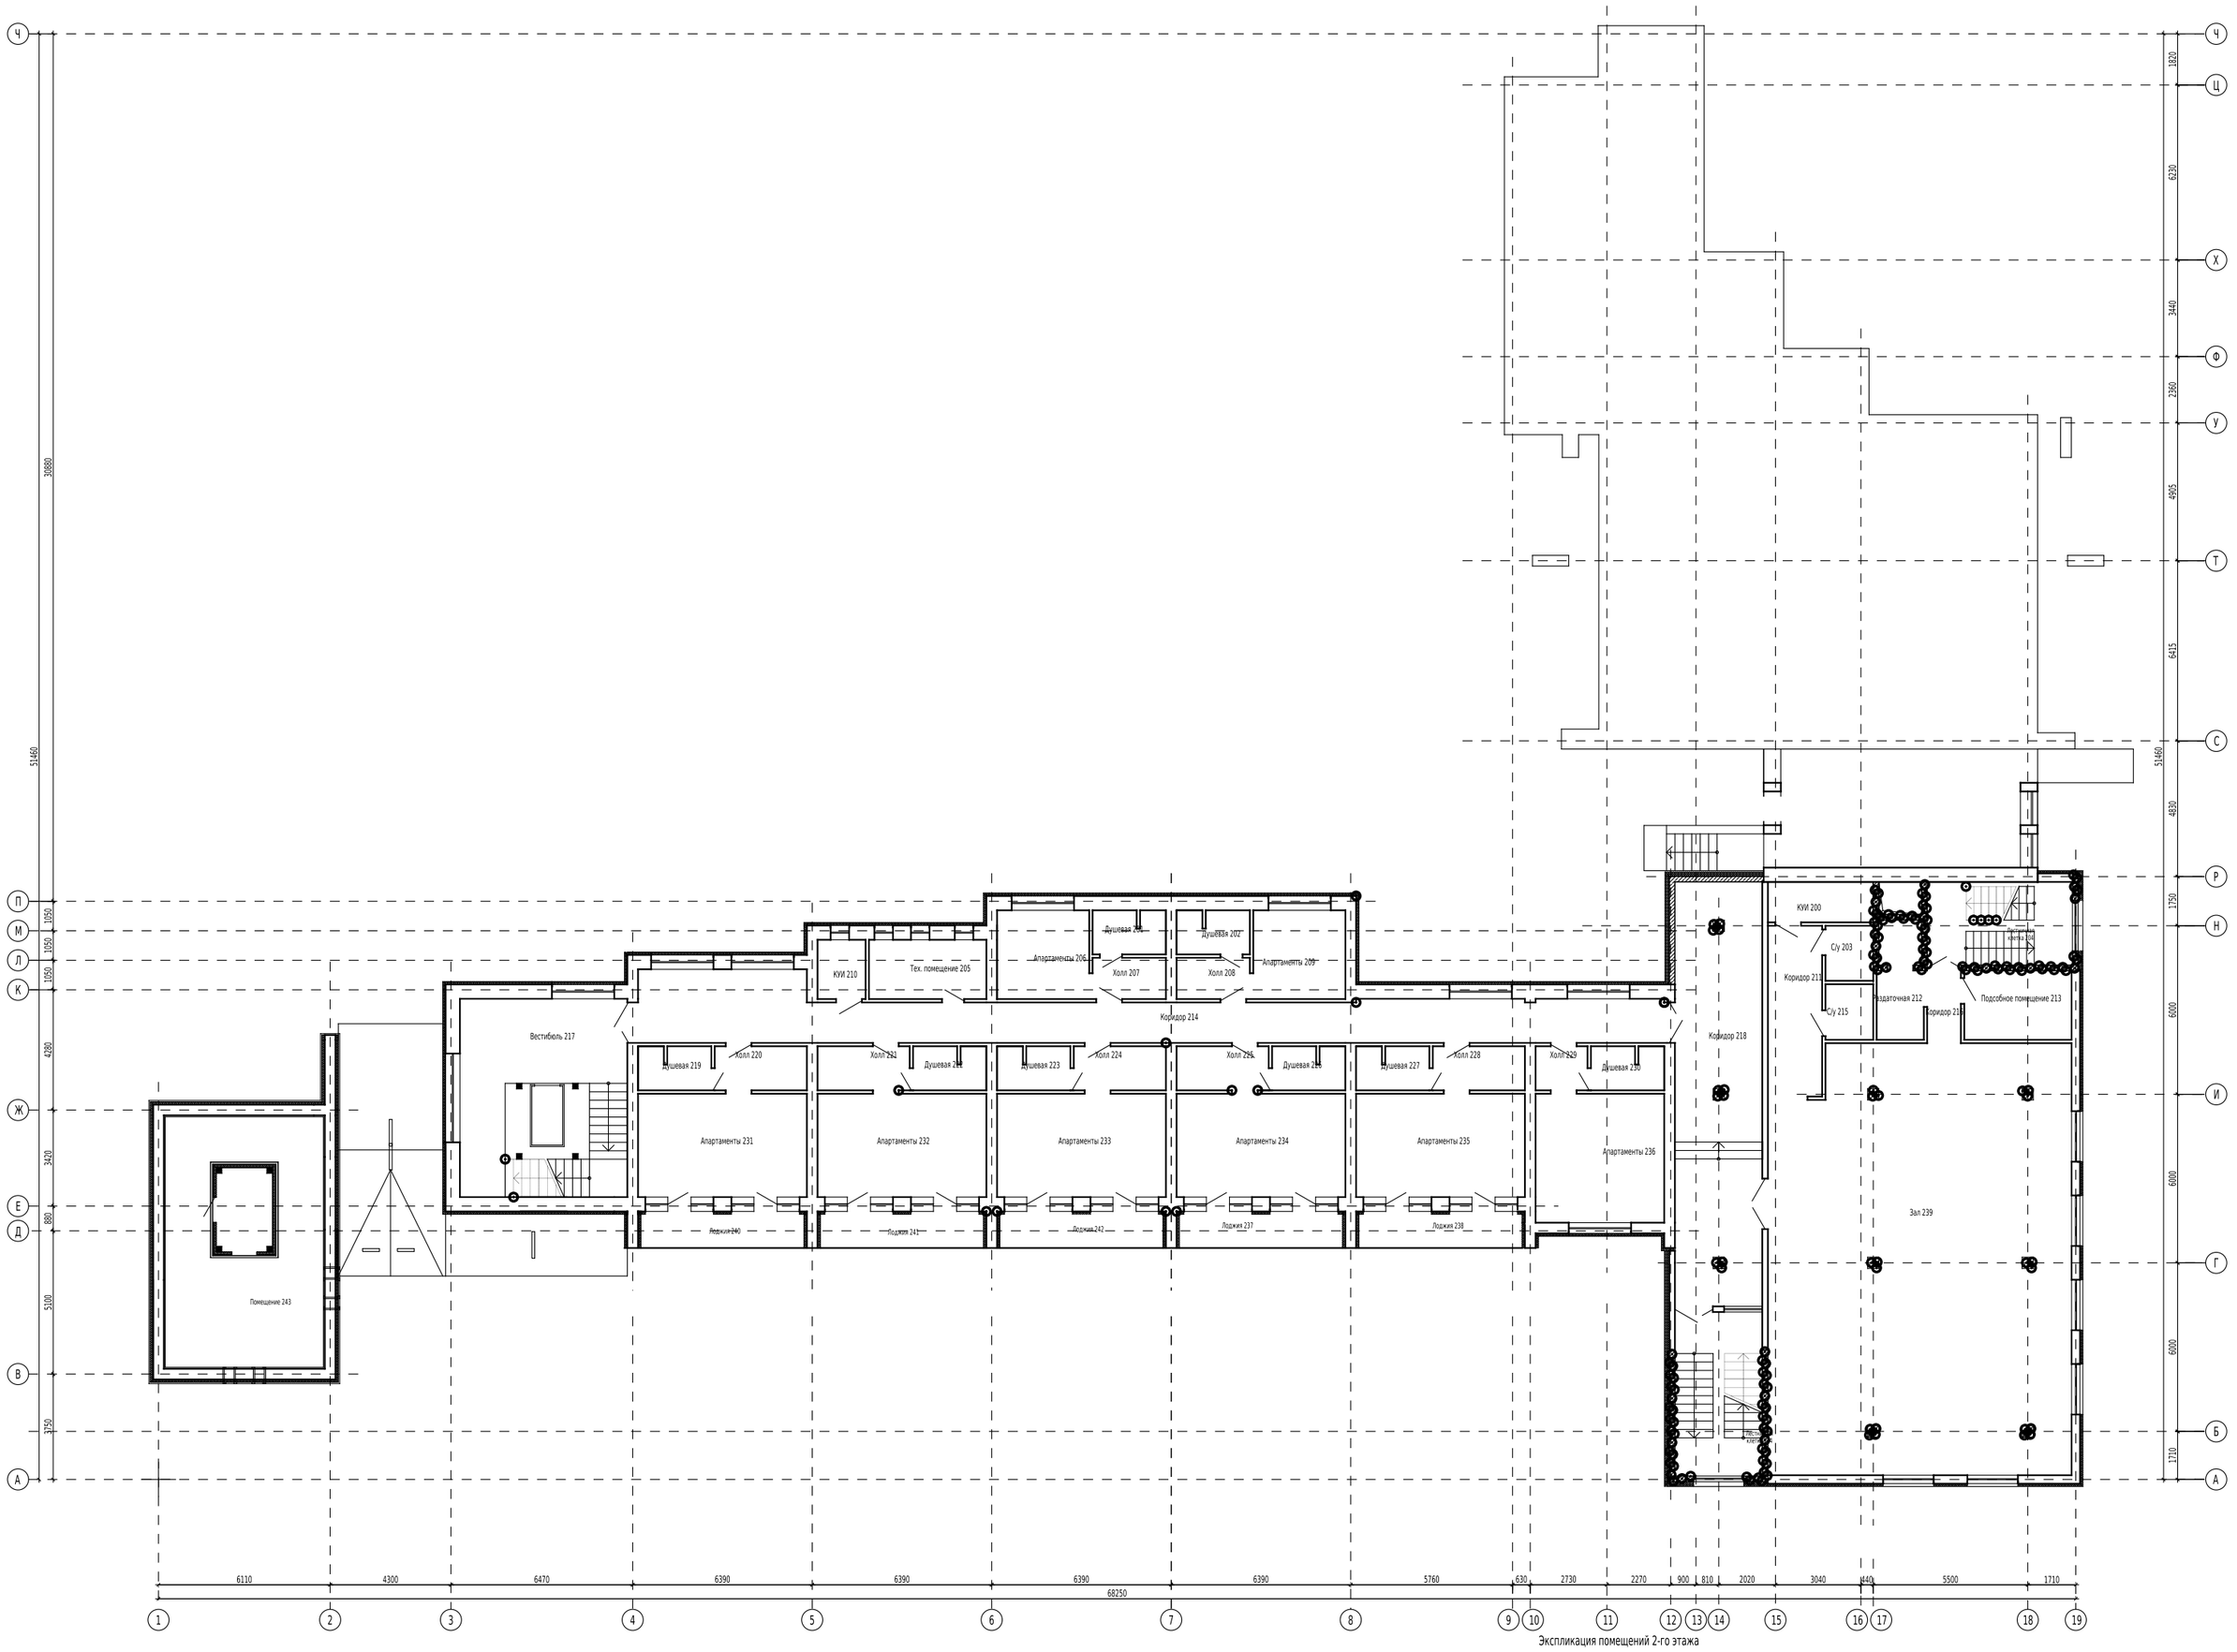

Экспликация помещений 2-го этажа

№	Наименование помещения	№	Наименование помещения	№	Наименование помещения	№	Наименование помещения
200	КУИ	212	Раздаточная	224	Холл	236	Апартаменты
201	Душевая	213	Подсобное помещение	225	Холл	237	Лоджия
202	Душевая	214	Коридор	226	Душевая	238	Лоджия
203	С/у	215	С/у	227	Душевая	239	Зал
204	Лестничная клетка	216	Коридор	228	Холл	240	Лоджия
205	Тех. помещение	217	Вестибюль	229	Холл	241	Лоджия
206	Апартаменты	218	Коридор	230	Душевая	242	Лоджия
207	Холл	219	Душевая	231	Апартаменты	243	Помещение
208	Холл	220	Холл	232	Апартаменты	244	Лестничная клетка
209	Апартаменты	221	Холл	233	Апартаменты		
210	КУИ	222	Душевая	234	Апартаменты		
211	Коридор	223	Душевая	235	Апартаменты		

1) Неуказанные диаметры трубопроводов системы отопления 20х2.8мм
2) Размещение радиаторов и полотенцесушителей уточнить по месту.
3) Трубопроводы отнесены от наружных стен условно, прокладку осуществить в полу и штробах.
4) На радиаторах установить вентили с термоголовками.
5) В местах прохода трубопроводами стен, перегородок установить стальные гильзы.

Взам. инв. N

Подпись и дата

Инв. N подл.

План 3-1 этажа

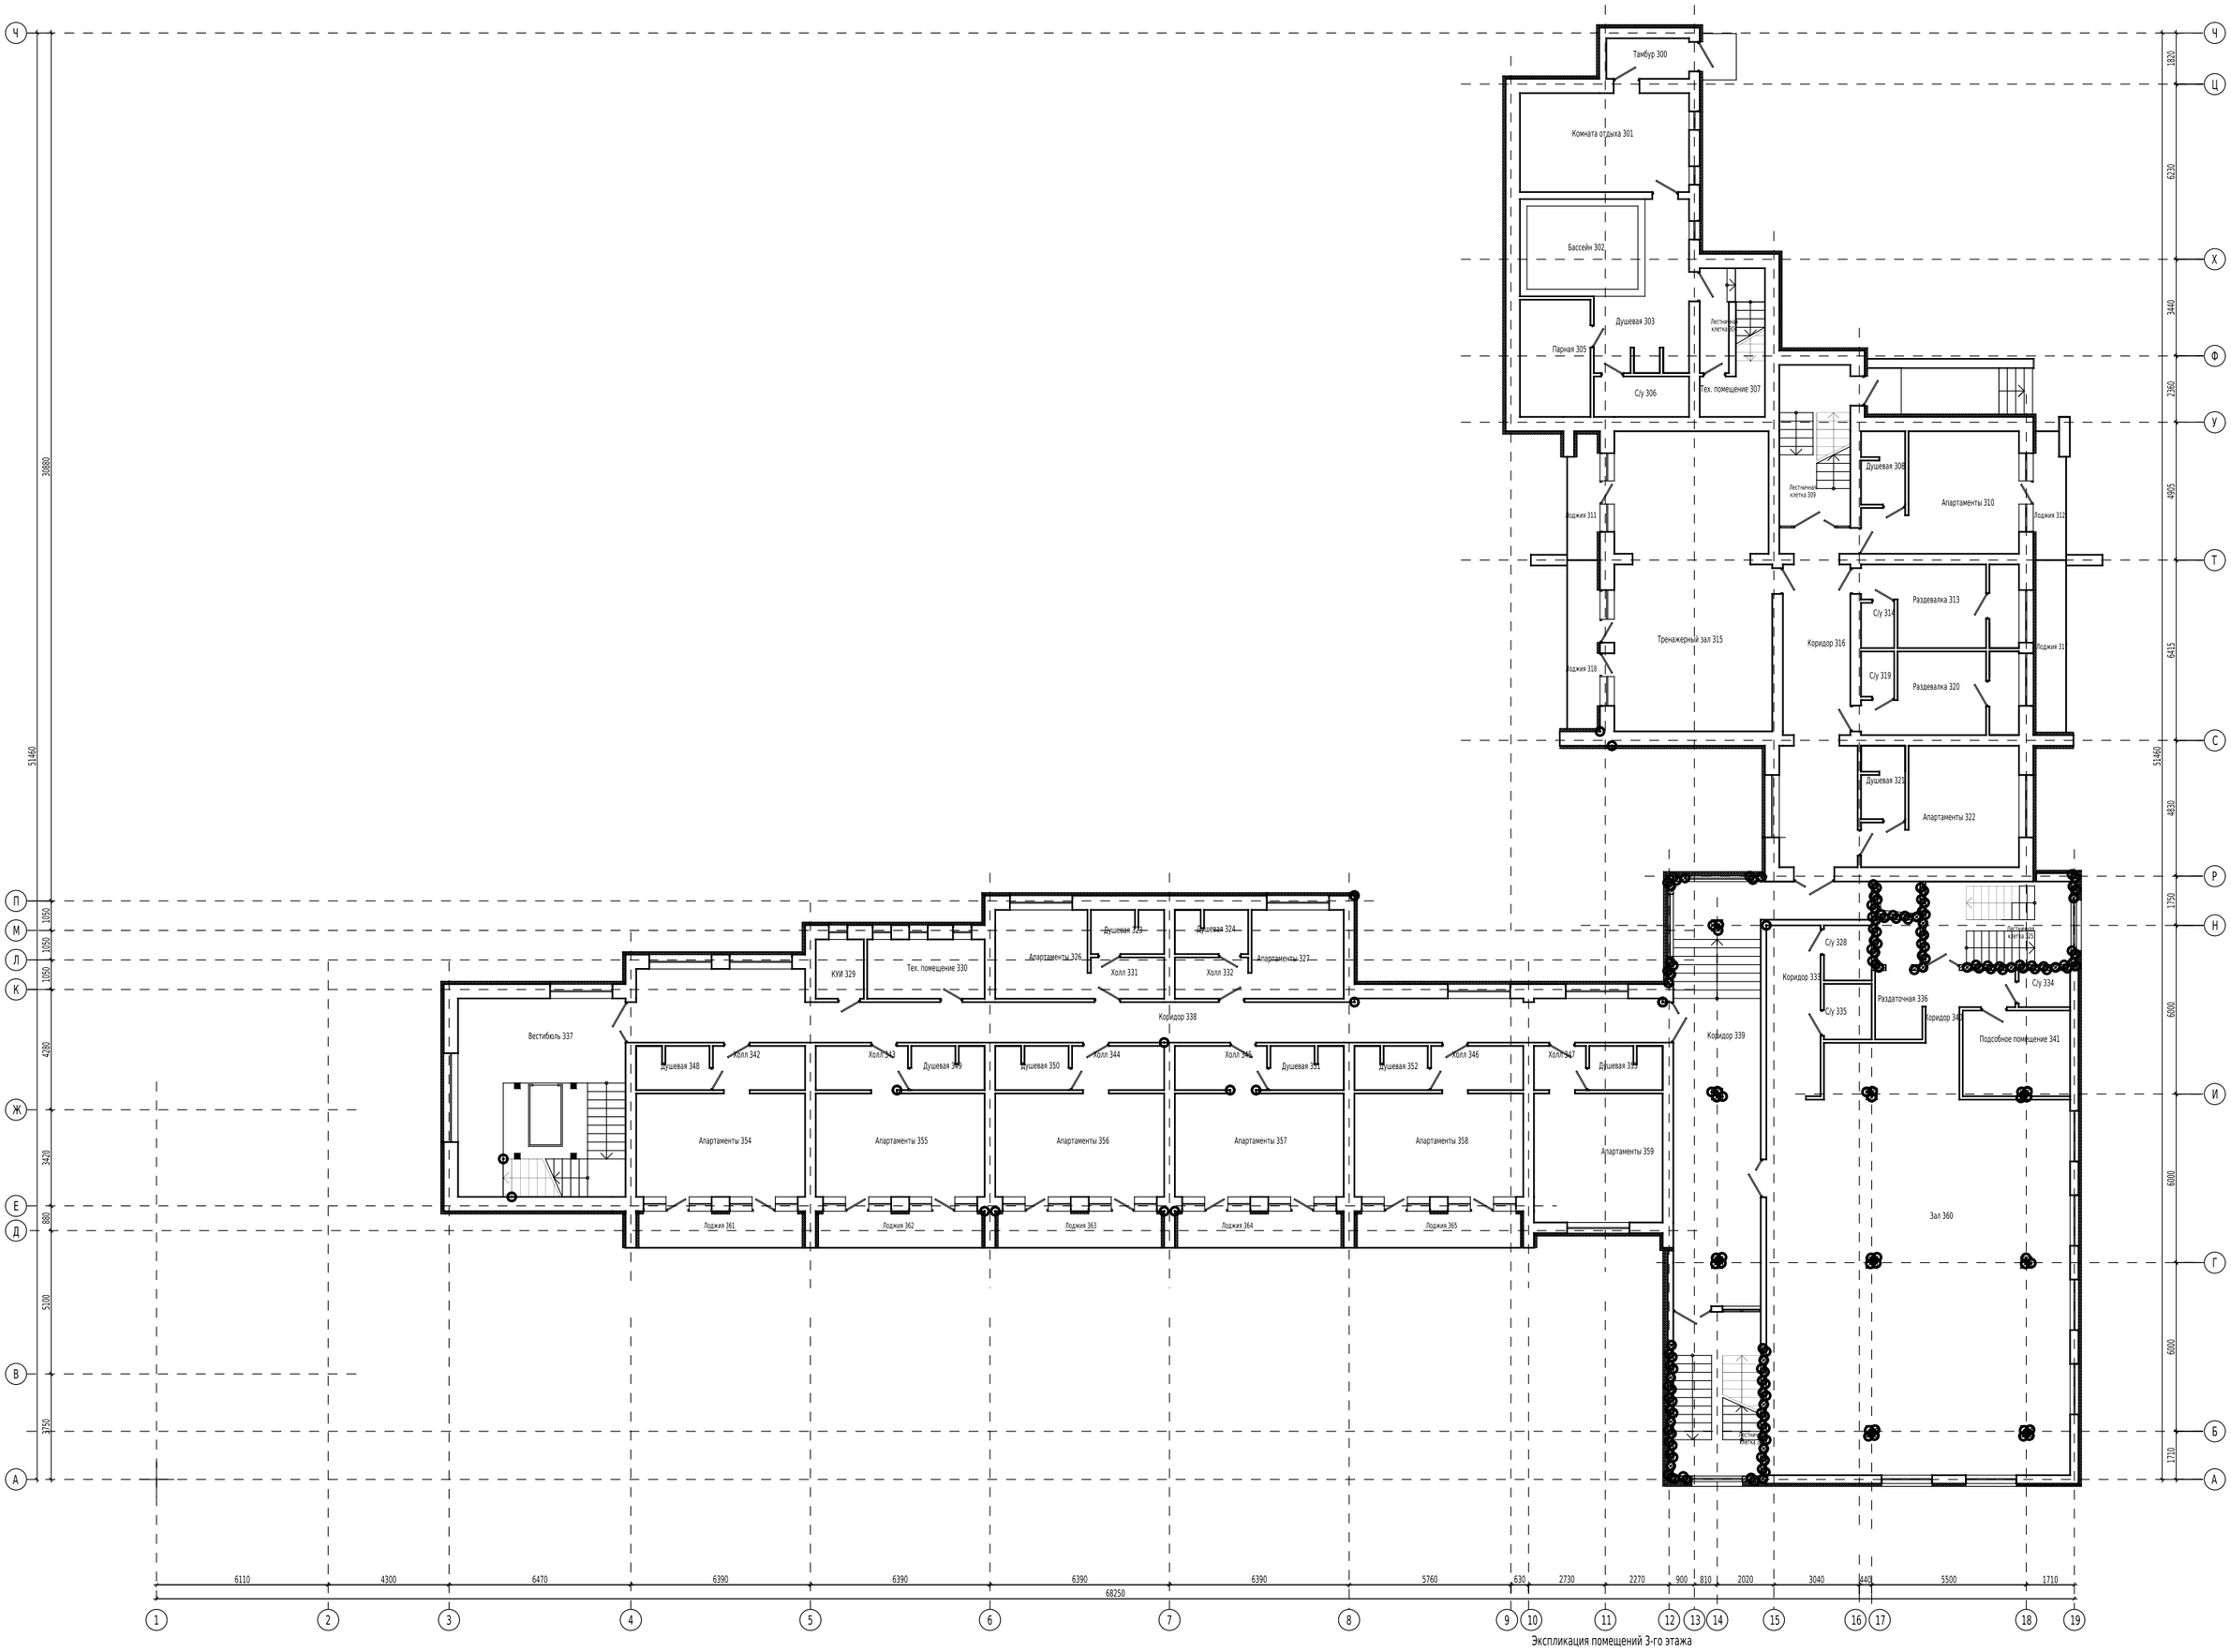

Экспликация помещений 3-го этажа

№	Наименование помещения	№	Наименование помещения	№	Наименование помещения	№	Наименование помещения
300	Тамбур	317	Лоджия	334	С/у	351	Душевая
301	Комната отдыха	318	Лоджия	335	С/у	352	Душевая
302	Бассейн	319	С/у	336	Раздаточная	353	Душевая
303	Душевая	320	Раздевалка	337	Вестибюль	354	Апартаменты
304	Лестничная клетка	321	Душевая	338	Коридор	355	Апартаменты
305	Парная	322	Апартаменты	339	Коридор	356	Апартаменты
306	С/у	323	Душевая	340	Коридор	357	Апартаменты
307	Тех. помещение	324	Душевая	341	Подсобное помещение	358	Апартаменты
308	Душевая	325	Лестничная клетка	342	Холл	359	Апартаменты
309	Лестничная клетка	326	Апартаменты	343	Холл	360	Зал
310	Апартаменты	327	Апартаменты	344	Холл	361	Лоджия
311	Лоджия	328	С/у	345	Холл	362	Лоджия
312	Лоджия	329	КУИ	346	Холл	363	Лоджия
313	Раздевалка	330	Тех. помещение	347	Холл	364	Лоджия
314	С/у	331	Холл	348	Душевая	365	Лоджия
315	Тренажерный зал	332	Холл	349	Душевая	366	Лестничная клетка
316	Коридор	333	Коридор	350	Душевая		

1) Неуказанные диаметры трубопроводов системы отопления 20х2.8мм
2) Размещение радиаторов и полотенцесушителей уточнить по месту.
3) Трубопроводы отнесены от наружных стен условно, прокладку осуществить в полу и штробах.
4) На радиаторах установить вентили с термоголовками.
5) В местах прохода трубопроводами стен, перегородок установить стальные гильзы.

Взам. инв. N
Подпись и дата
Инв. N подл.

План 4-2 этажа

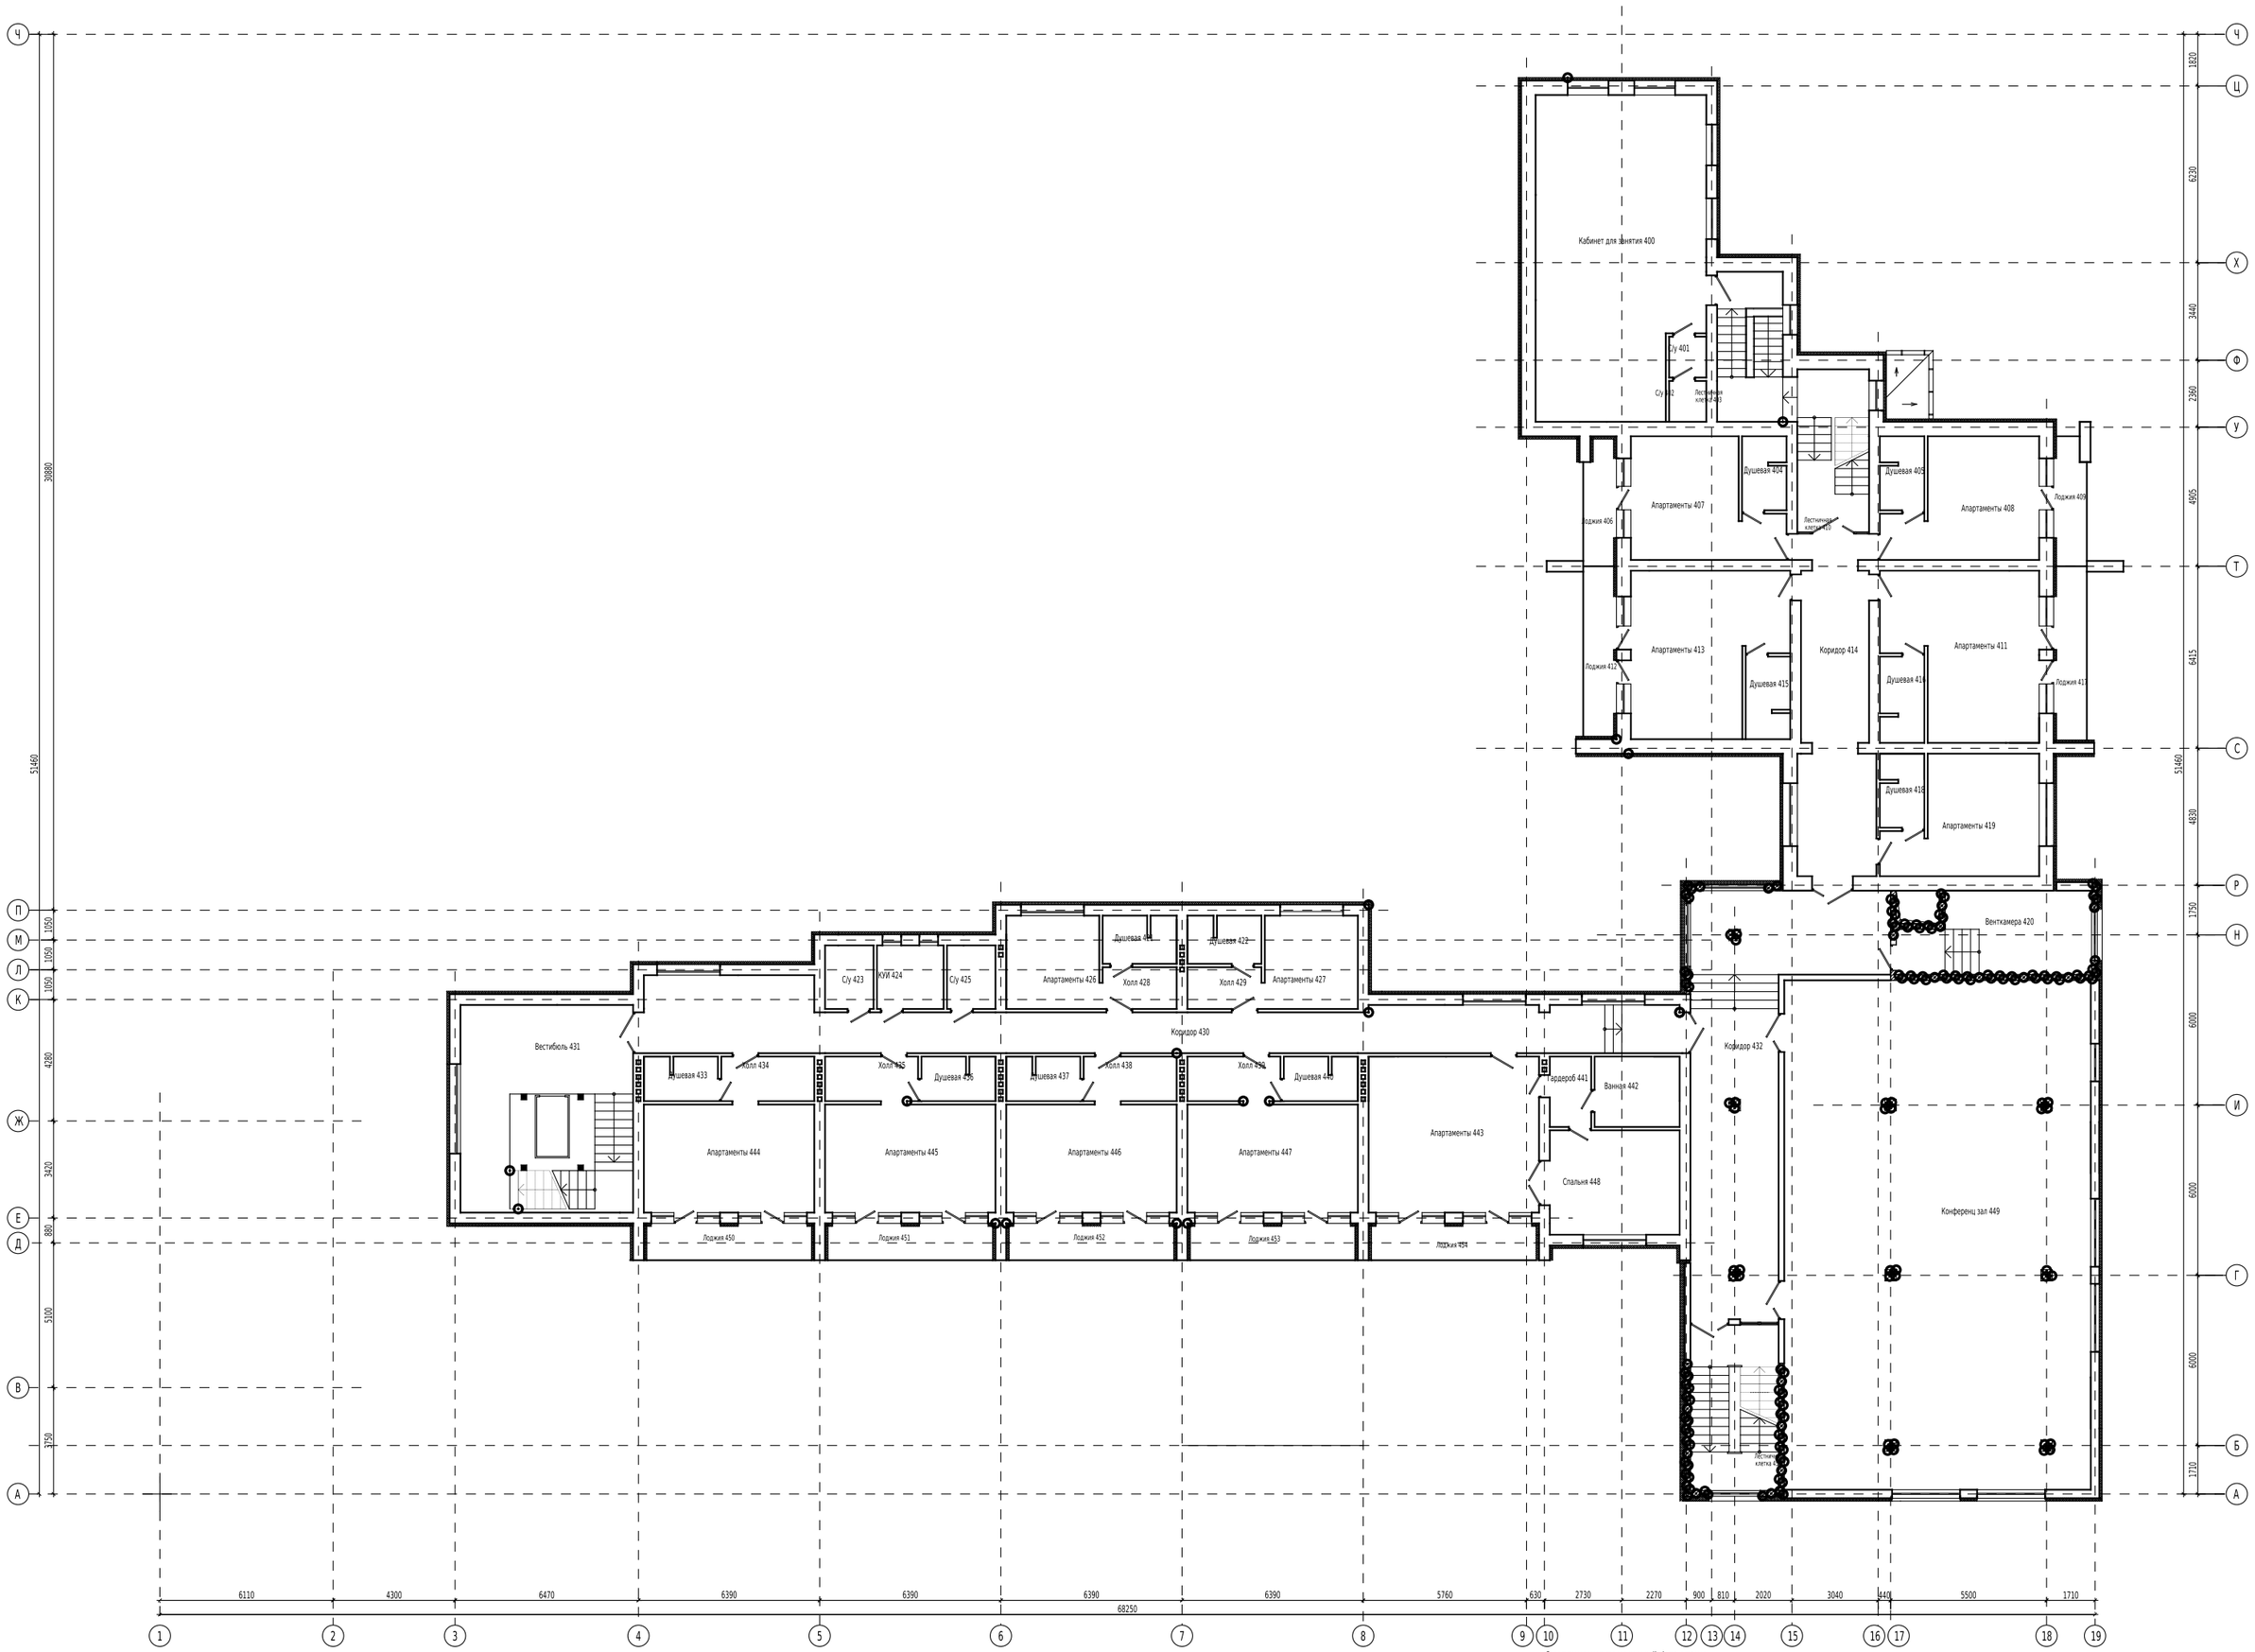

Экспликация помещений 4-го этажа

№	Наименование помещения	№	Наименование помещения	№	Наименование помещения	№	Наименование помещения
400	Кабинет для занятия	414	Коридор	428	Холл	442	Ванная
401	С/у	415	Душевая	429	Холл	443	Апартаменты
402	С/у	416	Душевая	430	Коридор	444	Апартаменты
403	Лестничная клетка	417	Лоджия	431	Вестибюль	445	Апартаменты
404	Душевая	418	Душевая	432	Коридор	446	Апартаменты
405	Душевая	419	Апартаменты	433	Душевая	447	Апартаменты
406	Лоджия	420	Венткамера	434	Холл	448	Спальня
407	Апартаменты	421	Душевая	435	Холл	449	Конференц зал
408	Апартаменты	422	Душевая	436	Душевая	450	Лоджия
409	Лоджия	423	С/у	437	Душевая	451	Лоджия
410	Лестничная клетка	424	КУИ	438	Холл	452	Лоджия
411	Апартаменты	425	С/у	439	Холл	453	Лоджия
412	Лоджия	426	Апартаменты	440	Душевая	454	Лоджия
413	Апартаменты	427	Апартаменты	441	Гардероб	455	Лестничная клетка

1) Неуказанные диаметры трубопроводов системы отопления 20х2.8мм
2) Размещение радиаторов и полотенцесушителей уточнить по месту.
3) Трубопроводы отнесены от наружных стен условно, прокладку осуществить в полу и штробах.
4) На радиаторах установить вентили с термоголовками.
5) В местах прохода трубопроводами стен, перегородок установить стальные гильзы.

Взам. инв. N
Подпись и дата
Инв. N подл.